CÔNG TY TNHH THƯƠNG MẠI VÀ XÂY DỰNG PV INCONS

Địa chỉ: Số P007, đường Lý Thái Tổ, phường Hưng Phú, Tp. Cần Thơ

Điện thoại: 0772 194 789 MST: 1501112147

Website: www.pvincons.com Email: pvincons@gmail.com

HỒ SƠ THIẾT KẾ

CÔNG TRÌNH: NHÀ Ở RIÊNG LẺ

ĐỊA CHỈ: THỬA ĐẤT SỐ 1299, TỜ BẢN ĐỒ SỐ 10, ẤP TRƯỜNG THỌ 2, XÃ TRƯỜNG LONG, THÀNH PHỐ CẦN THƠ


CHỦ ĐẦU TƯ: HÀ THU THẢO

03/08/2026

GHI CHÚ:

NHÀ ĐỀ NGHỊ CẤP GIẤY PHÉP XÂY DỰNG MỚI


- ĐỊA ĐIỂM XÂY DỰNG: THỬA ĐẤT 1299, TỜ BẢN ĐỒ SỐ10, ẤP TRƯỜNG THỌ 2, XÃ TRƯỜNG LONG, THÀNH PHỐ CẦN THƠ
- CẤU TRÚC: NHÀ KIÊN CỐ CẤP IV, TRỆT, MÁI TOLE + BÊ TÔNG CỐT THÉP, CỘT KHUNG SÀN BẰNG BÊ TÔNG CỐT THÉP ĐỔ TẠI CHỖ.
- DIỆN TÍCH KHU ĐẤT: 179,0 M2
- TRONG ĐÓ:
  + DIỆN TÍCH XÂY DỰNG : 5,0 x 20,0 = 100,0 M2
  + MẬT ĐỘ XÂY DỰNG: 56%
  + TỔNG DIỆN TÍCH SÀN : 100,0 M2
- CHIỀU CAO CÔNG TRÌNH : 5,55 M

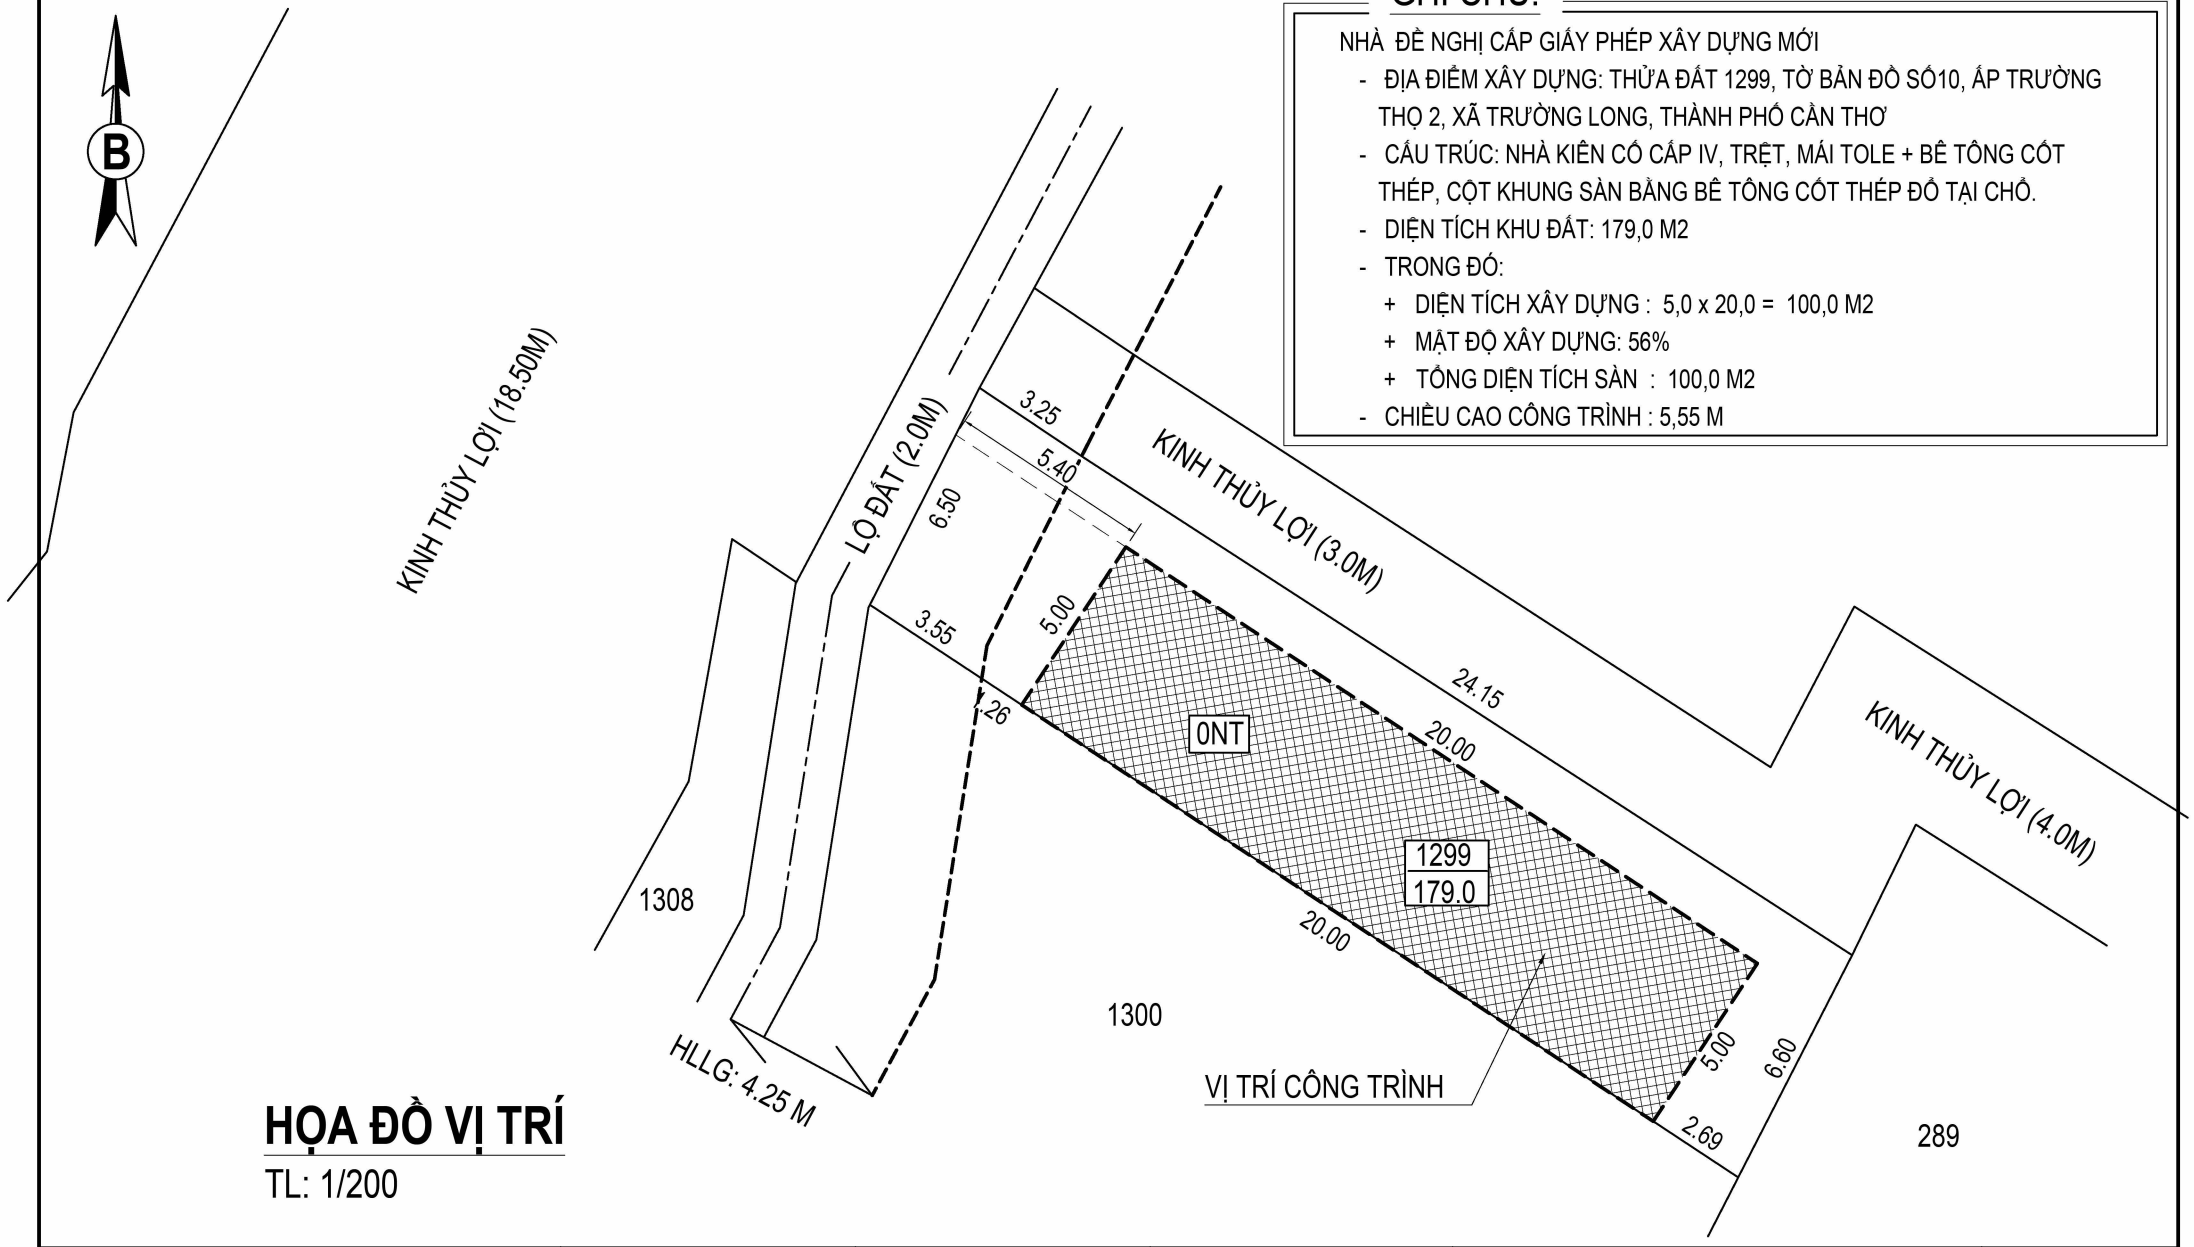

HỌA ĐỒ VỊ TRÍ

TL: 1/200


CÔNG TY TNHH THƯƠNG MẠI VÀ XÂY DỰNG PV INCONS Địa chỉ: P007, Đường Lý Thái Tổ, phường Hưng Phú, thành phố Cần Thơ Điện thoại: (+84) 0722 194 789 - 0939 751 194	GIÁM ĐỐC: TRẦN HOÀNG PHƯỚC	THIẾT KẾ: KS. TRẦN HOÀNG PHƯỚC	CHỦ ĐẦU TƯ: HÀ THU THẢO	CÔNG TRÌNH: NHÀ Ở RIÊNG LẺ ĐỊA ĐIỂM XÂY DỰNG: THỬA ĐẤT SỐ 1299, TỜ BẢN ĐỒ SỐ 10, ẤP TRƯỜNG THỌ 2, XÃ TRƯỜNG LONG, THÀNH PHỐ CẦN THƠ	TỶ LỆ: A4 - 1:1 NGÀY: 03/08/2026 SỐ BẢN VẼ: CP-01

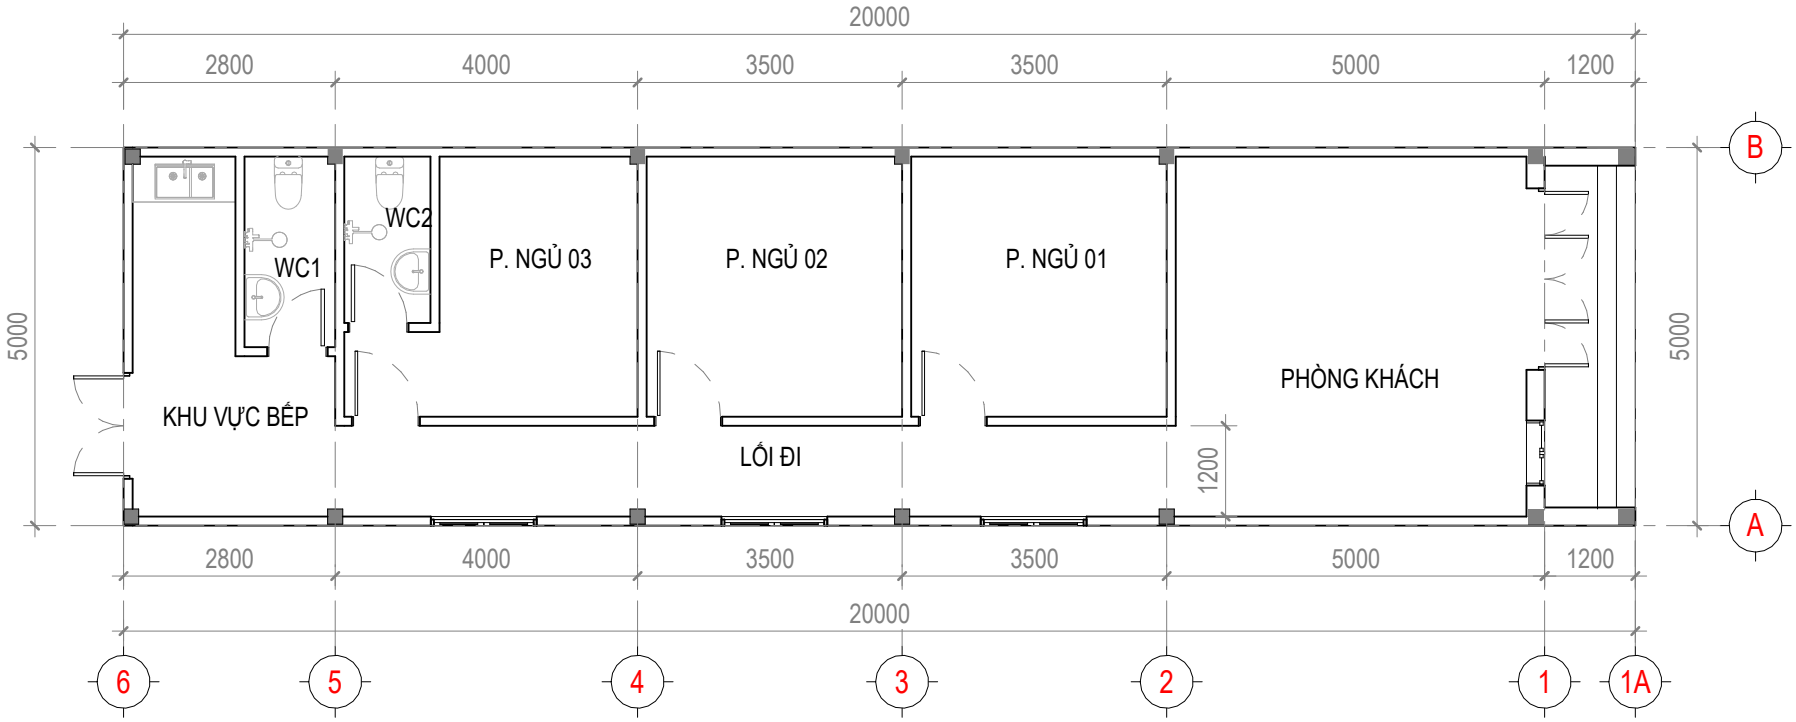

MẶT BẰNG TẦNG TRỆT

TL 1 : 100

CÔNG TY TNHH THƯƠNG MẠI VÀ XÂY DỰNG PV INCONS Địa chỉ: P007, Đường Lý Thái Tổ, phường Hưng Phú, thành phố Cần Thơ Điện thoại: (+84) 0722 194 789 - 0939 751 194	GIÁM ĐỐC: TRẦN HOÀNG PHƯỚC	THIẾT KẾ: KS. TRẦN HOÀNG PHƯỚC	CHỦ ĐẦU TƯ: HÀ THU THẢO	CÔNG TRÌNH: NHÀ Ở RIÊNG LẺ ĐỊA ĐIỂM XÂY DỰNG: THỬA ĐẤT SỐ 1299, TỜ BẢN ĐỒ SỐ 10, ẤP TRƯỜNG THỌ 2, XÃ TRƯỜNG LONG, THÀNH PHỐ CẦN THƠ	TỶ LỆ: A4 - 1:1 NGÀY: 03/08/2026 SỐ BẢN VẼ: CP-02

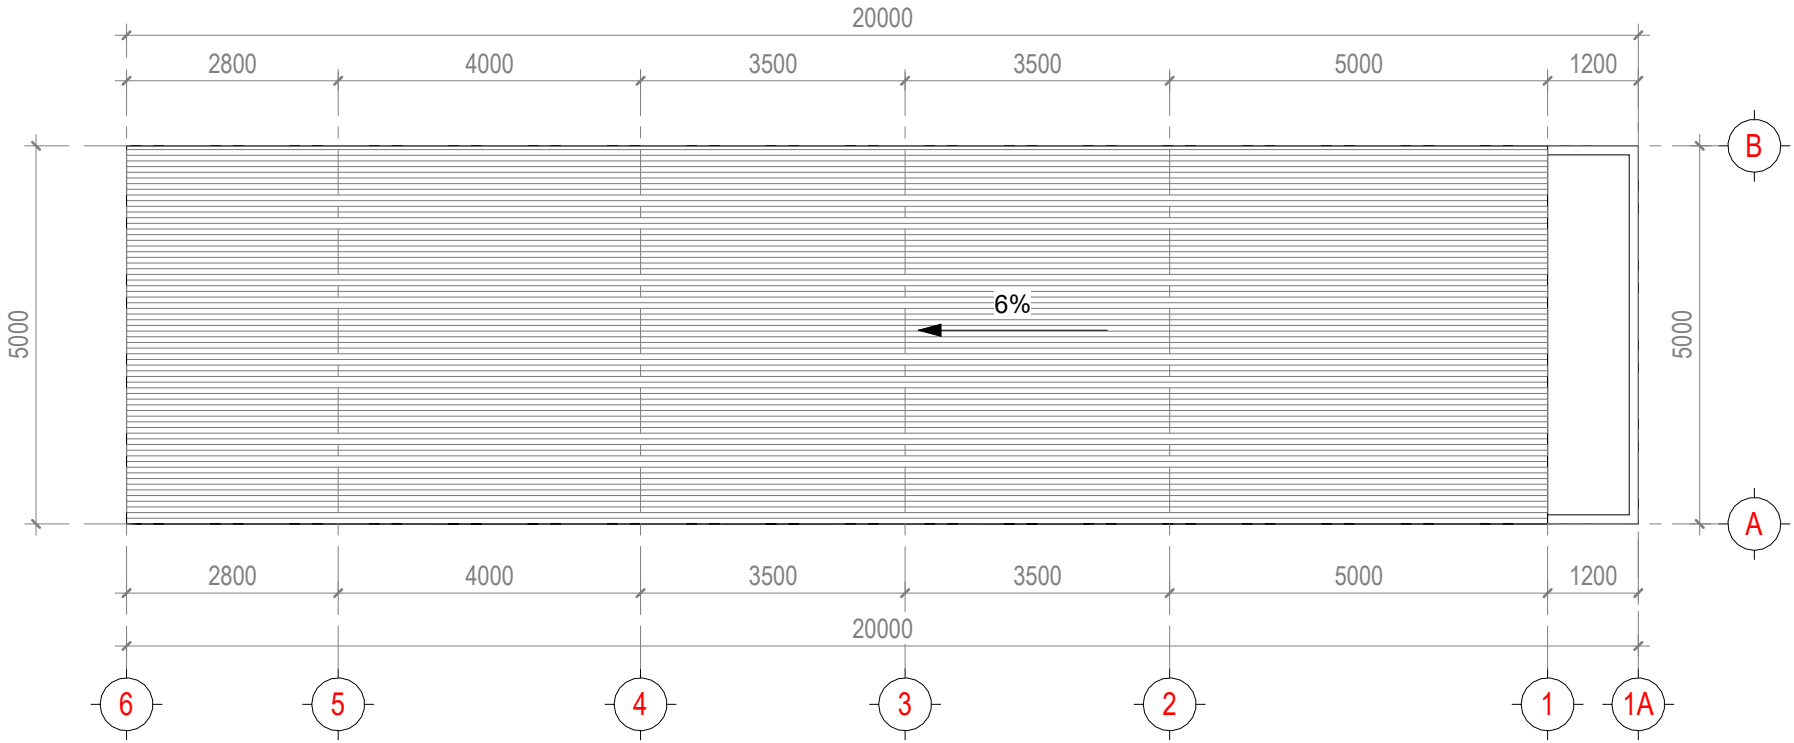

MẶT BẰNG MÁI


TL 1 : 100

CÔNG TY TNHH THƯƠNG MẠI VÀ XÂY DỰNG
PV INCONS

Địa chỉ: P007, Đường Lý Thái Tổ, phường Hưng Phú, thành phố Cần Thơ

Điện thoại: (+84) 0722 194 789 - 0939 751 194

GIÁM ĐỐC:	THIẾT KẾ:	CHỦ ĐẦU TƯ:	CÔNG TRÌNH:	TỶ LỆ:
TRẦN HOÀNG PHƯỚC	KS. TRẦN HOÀNG PHƯỚC	HÀ THU THẢO	NHÀ Ở RIÊNG LẺ ĐỊA ĐIỂM XÂY DỰNG: THỬA ĐẤT SỐ 1299, TỜ BẢN ĐỒ SỐ 10, ẤP TRƯỜNG THỌ 2, XÃ TRƯỜNG LONG, THÀNH PHỐ CẦN THƠ	A4 - 1:1 NGÀY: 03/08/2026 SỐ BẢN VẼ: CP-03

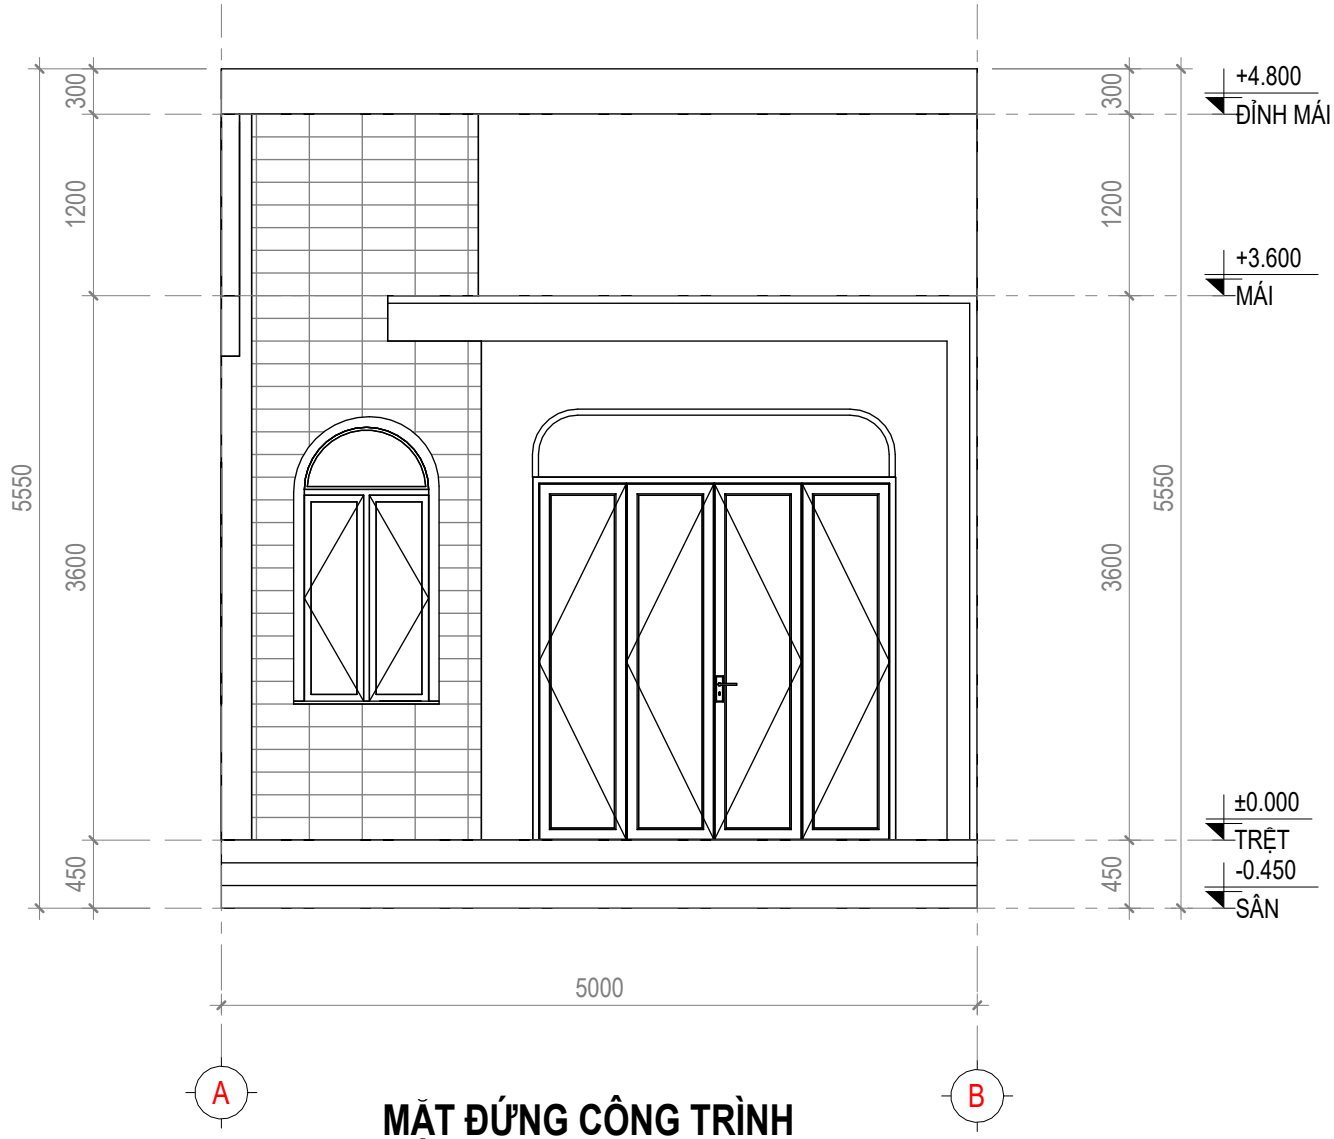

MẶT ĐỨNG CÔNG TRÌNH


TL 1 : 50

CÔNG TY TNHH THƯƠNG MẠI VÀ XÂY DỰNG
PV INCONS

Địa chỉ: P007, Đường Lý Thái Tổ, phường Hưng Phú, thành phố Cần Thơ

Điện thoại: (+84) 0722 194 789 - 0939 751 194


GIÁM ĐỐC:	THIẾT KẾ:	CHỦ ĐẦU TƯ:	CÔNG TRÌNH:	TỶ LỆ:
TRẦN HOÀNG PHƯỚC	KS. TRẦN HOÀNG PHƯỚC	HÀ THU THẢO	NHÀ Ở RIÊNG LẺ ĐỊA ĐIỂM XÂY DỰNG: THỬA ĐẤT SỐ 1299, TỜ BẢN ĐỒ SỐ 10, ẤP TRƯỜNG THỌ 2, XÃ TRƯỜNG LONG, THÀNH PHỐ CẦN THƠ	A4 - 1:1 NGÀY: 03/08/2026 SỐ BẢN VẼ: CP-04

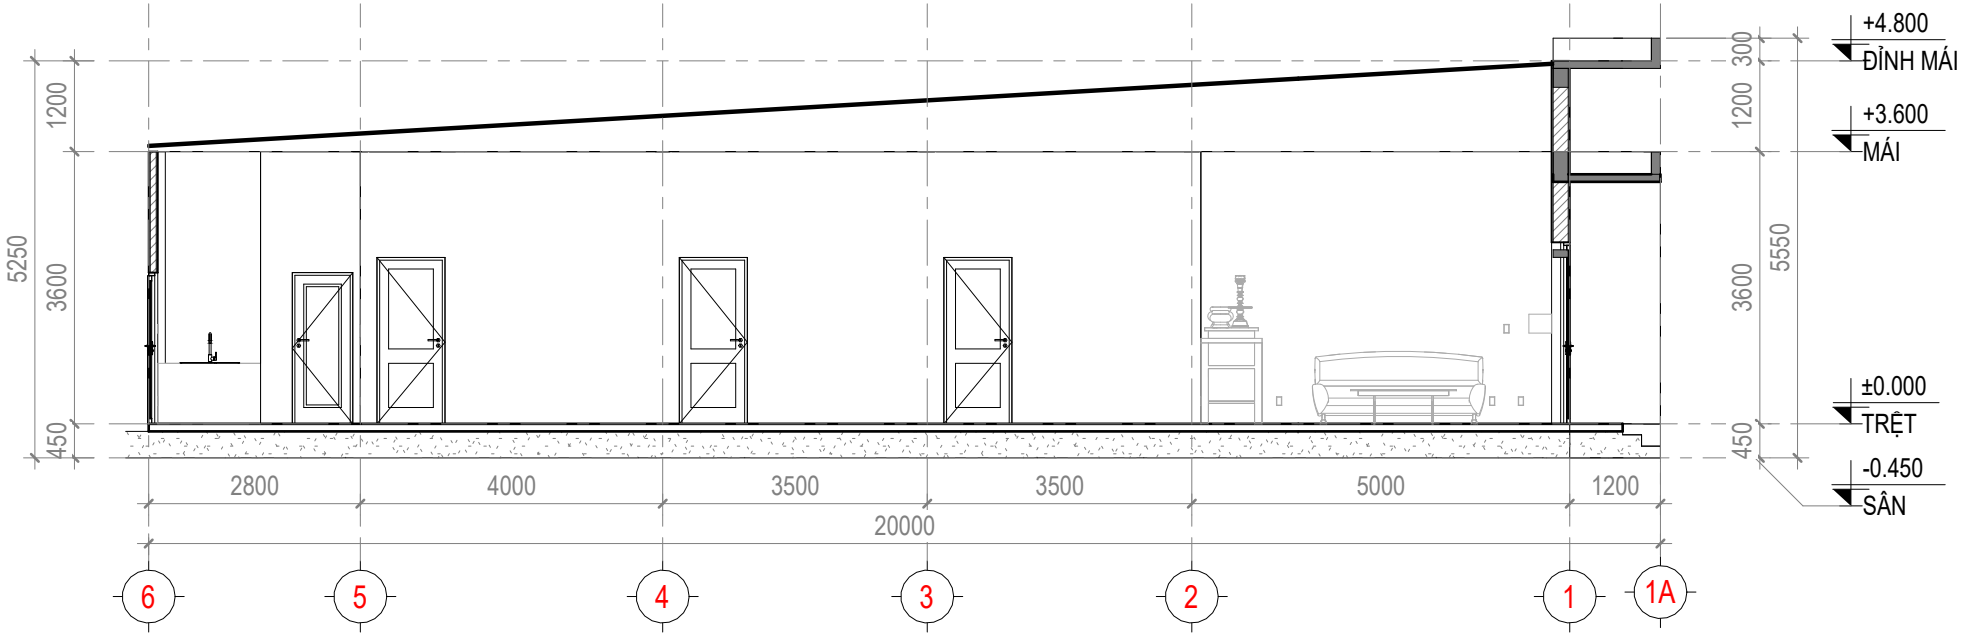

MẶT CẮT DỌC CÔNG TRÌNH


TL 1 : 100

CÔNG TY TNHH THƯƠNG MẠI VÀ XÂY DỰNG **PV INCONS** **Địa chỉ:** P007, Đường Lý Thái Tổ, phường Hưng Phú, thành phố Cần Thơ **Điện thoại:** (+84) 0722 194 789 - 0939 751 194	**GIÁM ĐỐC:** TRẦN HOÀNG PHƯỚC	**THIẾT KẾ:** KS. TRẦN HOÀNG PHƯỚC	**CHỦ ĐẦU TƯ:** HÀ THU THẢO	**CÔNG TRÌNH:** NHÀ Ở RIÊNG LẺ **ĐỊA ĐIỂM XÂY DỰNG:** THỬA ĐẤT SỐ 1299, TỜ BẢN ĐỒ SỐ 10, ẤP TRƯỜNG THỌ 2, XÃ TRƯỜNG LONG, THÀNH PHỐ CẦN THƠ	**TỶ LỆ:** A4 - 1:1 **NGÀY:** 03/08/2026 **SỐ BẢN VẼ:** CP-05

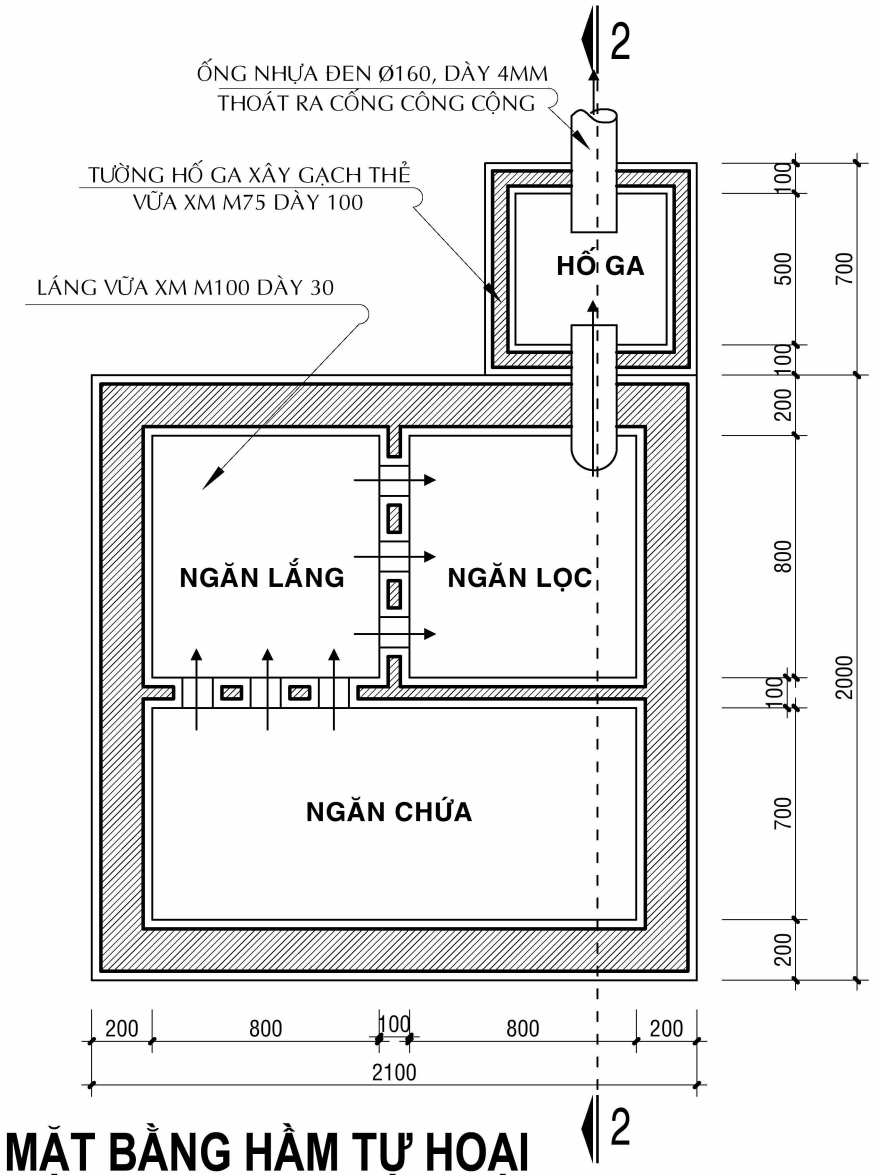

MẶT BẰNG HẦM TỰ HOẠI

TL: 1/100

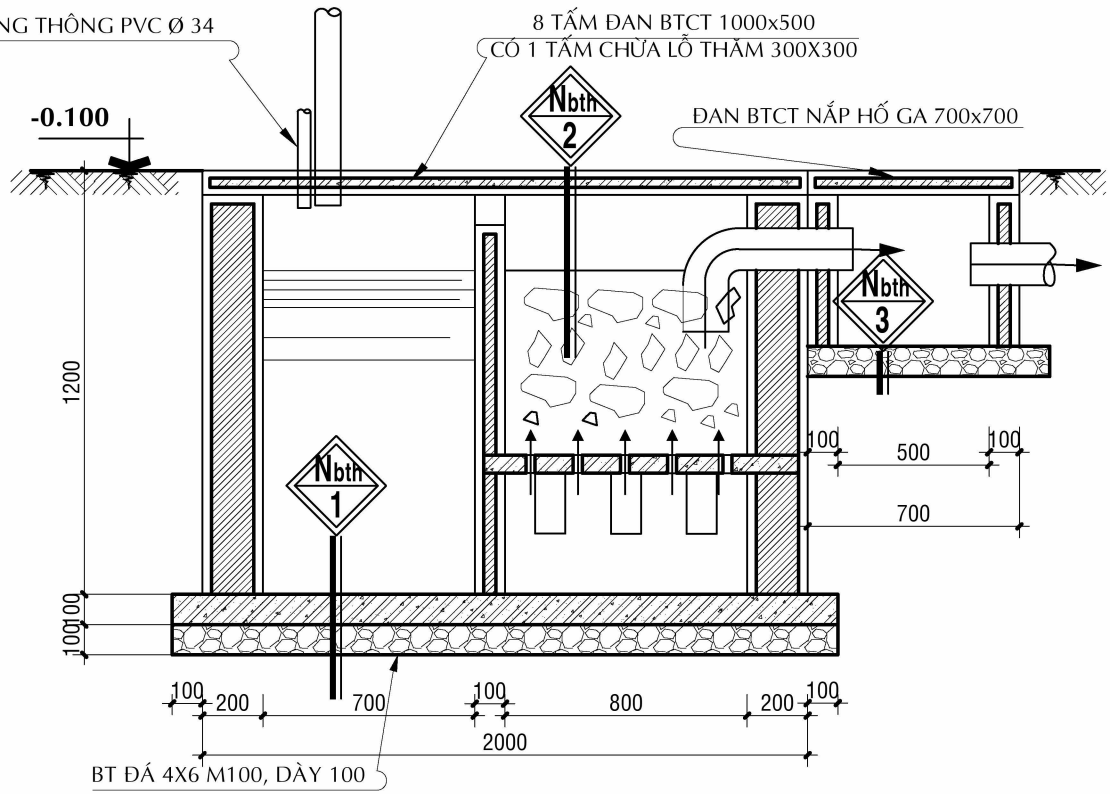

MẶT CẮT 2-2


TL: 1/100

CÔNG TY TNHH THƯƠNG MẠI VÀ XÂY DỰNG
PV INCONS

Địa chỉ: P007, Đường Lý Thái Tổ, phường Hưng Phú, thành phố Cần Thơ


Điện thoại: (+84) 0722 194 789 - 0939 751 194

GIÁM ĐỐC:	THIẾT KẾ:	CHỦ ĐẦU TƯ:	CÔNG TRÌNH:	TỶ LỆ:
TRẦN HOÀNG PHƯỚC	KS. TRẦN HOÀNG PHƯỚC	HÀ THU THẢO	NHÀ Ở RIÊNG LẺ ĐỊA ĐIỂM XÂY DỰNG: THỬA ĐẤT SỐ 1299, TỜ BẢN ĐỒ SỐ 10, ẤP TRƯỜNG THỌ 2, XÃ TRƯỜNG LONG, THÀNH PHỐ CẦN THƠ	A4 - 1:1 NGÀY: 03/08/2026 SỐ BẢN VẼ: CP-06

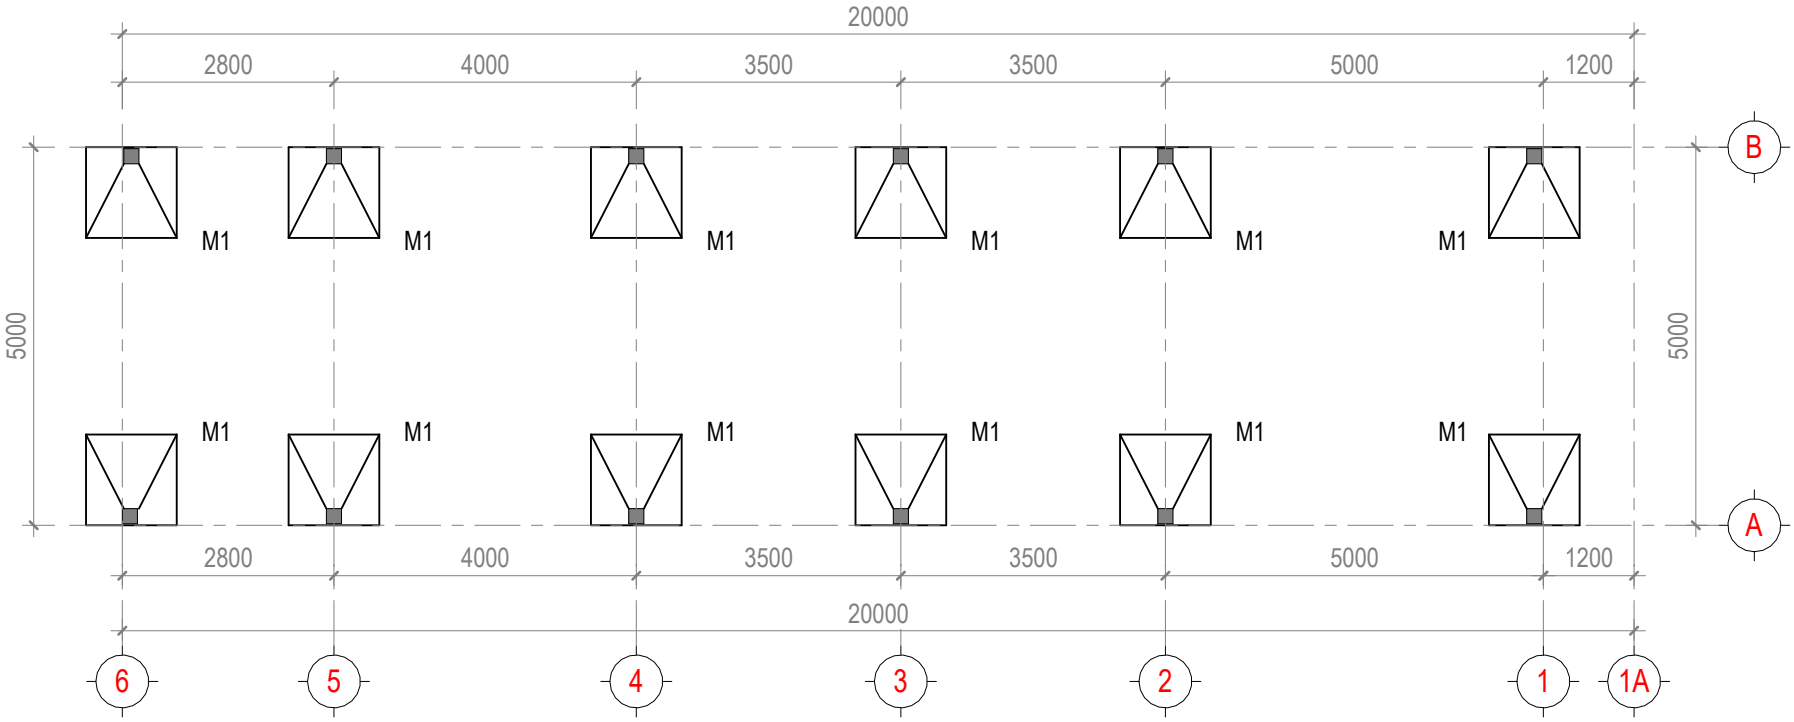


MẶT BẰNG MÓNG

TL 1 : 100

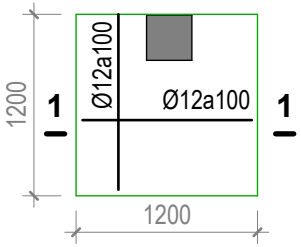


MẶT BẰNG MÓNG_TL: 1/50

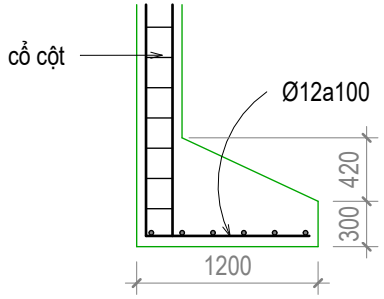

MẶT CẮT 1-1_TL: 1/50


CÔNG TY TNHH THƯƠNG MẠI VÀ XÂY DỰNG **PV INCONS** Địa chỉ: P007, Đường Lý Thái Tổ, phường Hưng Phú, thành phố Cần Thơ Điện thoại: (+84) 0722 194 789 - 0939 751 194	GIÁM ĐỐC: TRẦN HOÀNG PHƯỚC	THIẾT KẾ: KS. TRẦN HOÀNG PHƯỚC	CHỦ ĐẦU TƯ: HÀ THU THẢO	CÔNG TRÌNH: **NHÀ Ở RIÊNG LẺ** ĐỊA ĐIỂM XÂY DỰNG: THỬA ĐẤT SỐ 1299, TỜ BẢN ĐỒ SỐ 10, ẤP TRƯỜNG THỌ 2, XÃ TRƯỜNG LONG, THÀNH PHỐ CẦN THƠ	TỶ LỆ: A4 - 1:1 NGÀY: 03/08/2026 SỐ BẢN VẼ: CP-07

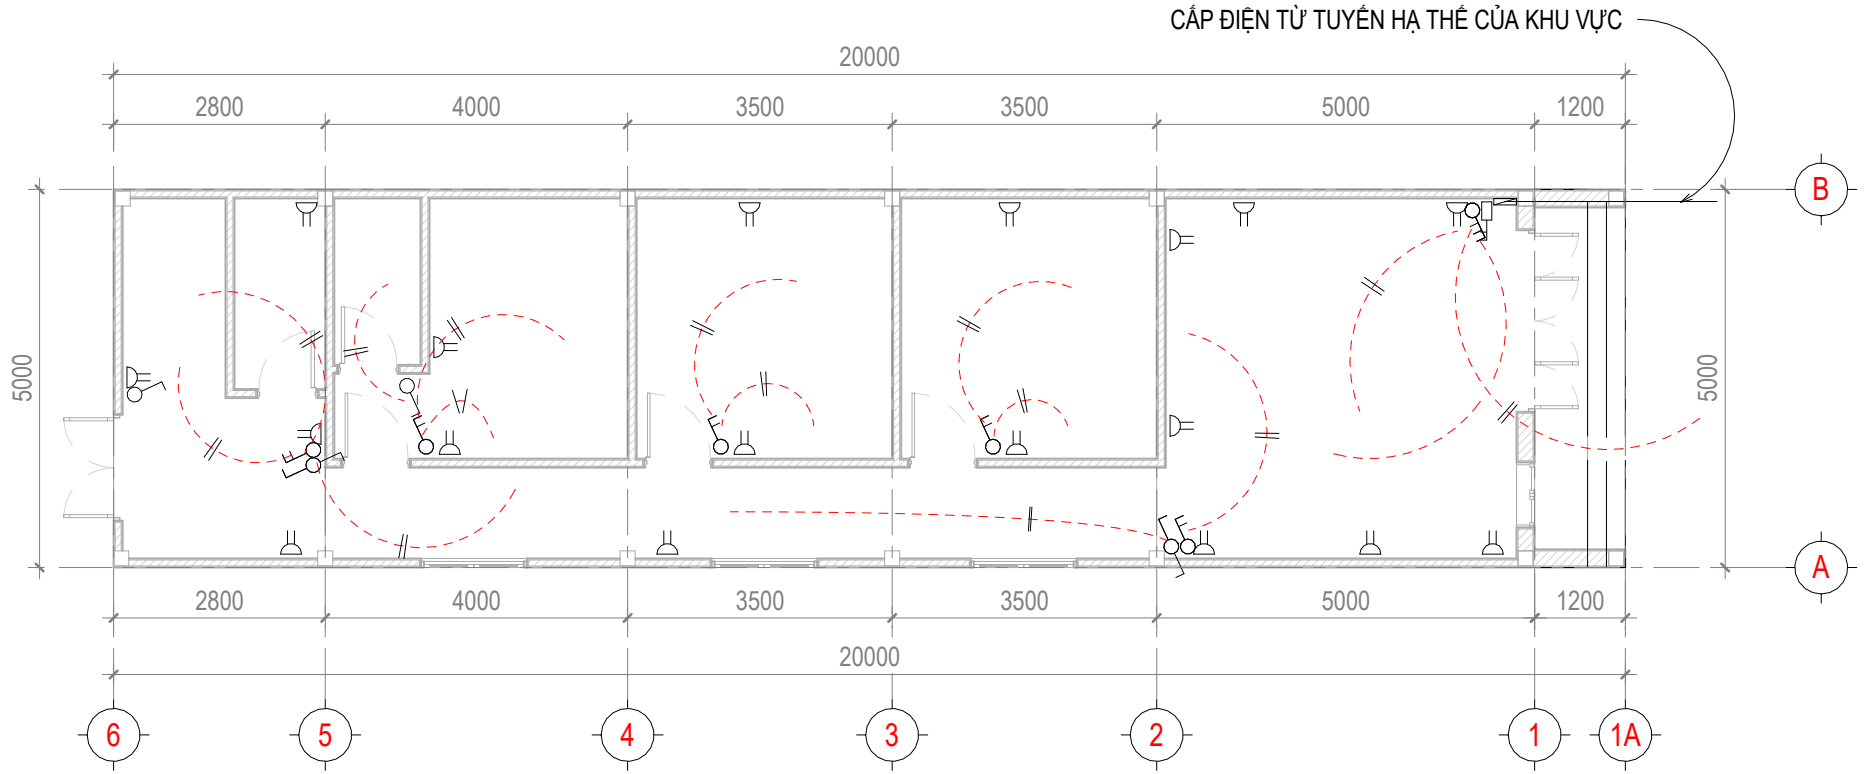

MẶT BẰNG CẤP ĐIỆN TẦNG TRỆT

TL 1 : 100


CÔNG TY TNHH THƯƠNG MẠI VÀ XÂY DỰNG PV INCONS Địa chỉ: P007, Đường Lý Thái Tổ, phường Hưng Phú, thành phố Cần Thơ Điện thoại: (+84) 0722 194 789 - 0939 751 194	GIÁM ĐỐC: TRẦN HOÀNG PHƯỚC	THIẾT KẾ: KS. TRẦN HOÀNG PHƯỚC	CHỦ ĐẦU TƯ: HÀ THU THẢO	CÔNG TRÌNH: NHÀ Ở RIÊNG LẺ ĐỊA ĐIỂM XÂY DỰNG: THỬA ĐẤT SỐ 1299, TỜ BẢN ĐỒ SỐ 10, ẤP TRƯỜNG THỌ 2, XÃ TRƯỜNG LONG, THÀNH PHỐ CẦN THƠ	TỶ LỆ: A4 - 1:1 NGÀY: 03/08/2026 SỐ BẢN VẼ: CP-08

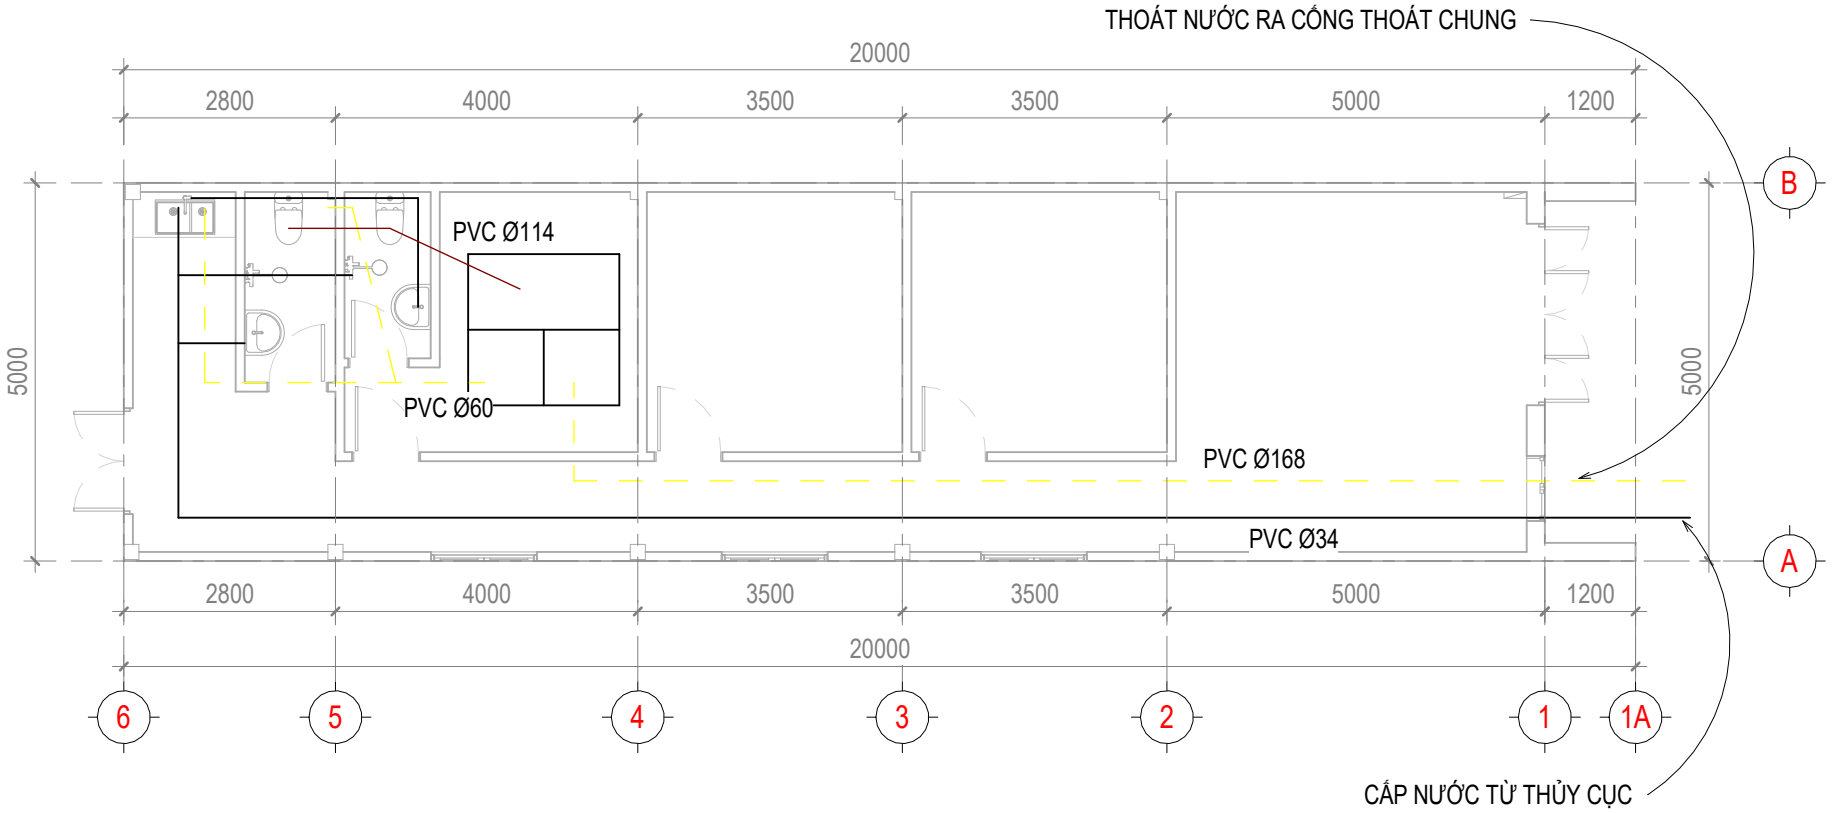

MẶT BẰNG CẤP THOÁT NƯỚC TẦNG TRỆT

TL 1 : 100

CÔNG TY TNHH THƯƠNG MẠI VÀ XÂY DỰNG **PV INCONS** Địa chỉ: P007, Đường Lý Thái Tổ, phường Hưng Phú, thành phố Cần Thơ Điện thoại: (+84) 0722 194 789 - 0939 751 194	GIÁM ĐỐC: TRẦN HOÀNG PHƯỚC	THIẾT KẾ: KS. TRẦN HOÀNG PHƯỚC	CHỦ ĐẦU TƯ: HÀ THU THẢO	CÔNG TRÌNH: **NHÀ Ở RIÊNG LẺ** ĐỊA ĐIỂM XÂY DỰNG: THỬA ĐẤT SỐ 1299, TỜ BẢN ĐỒ SỐ 10, ẤP TRƯỜNG THỌ 2, XÃ TRƯỜNG LONG, THÀNH PHỐ CẦN THƠ	TỶ LỆ: A4 - 1:1 NGÀY: 03/08/2026 SỐ BẢN VẼ: CP-09

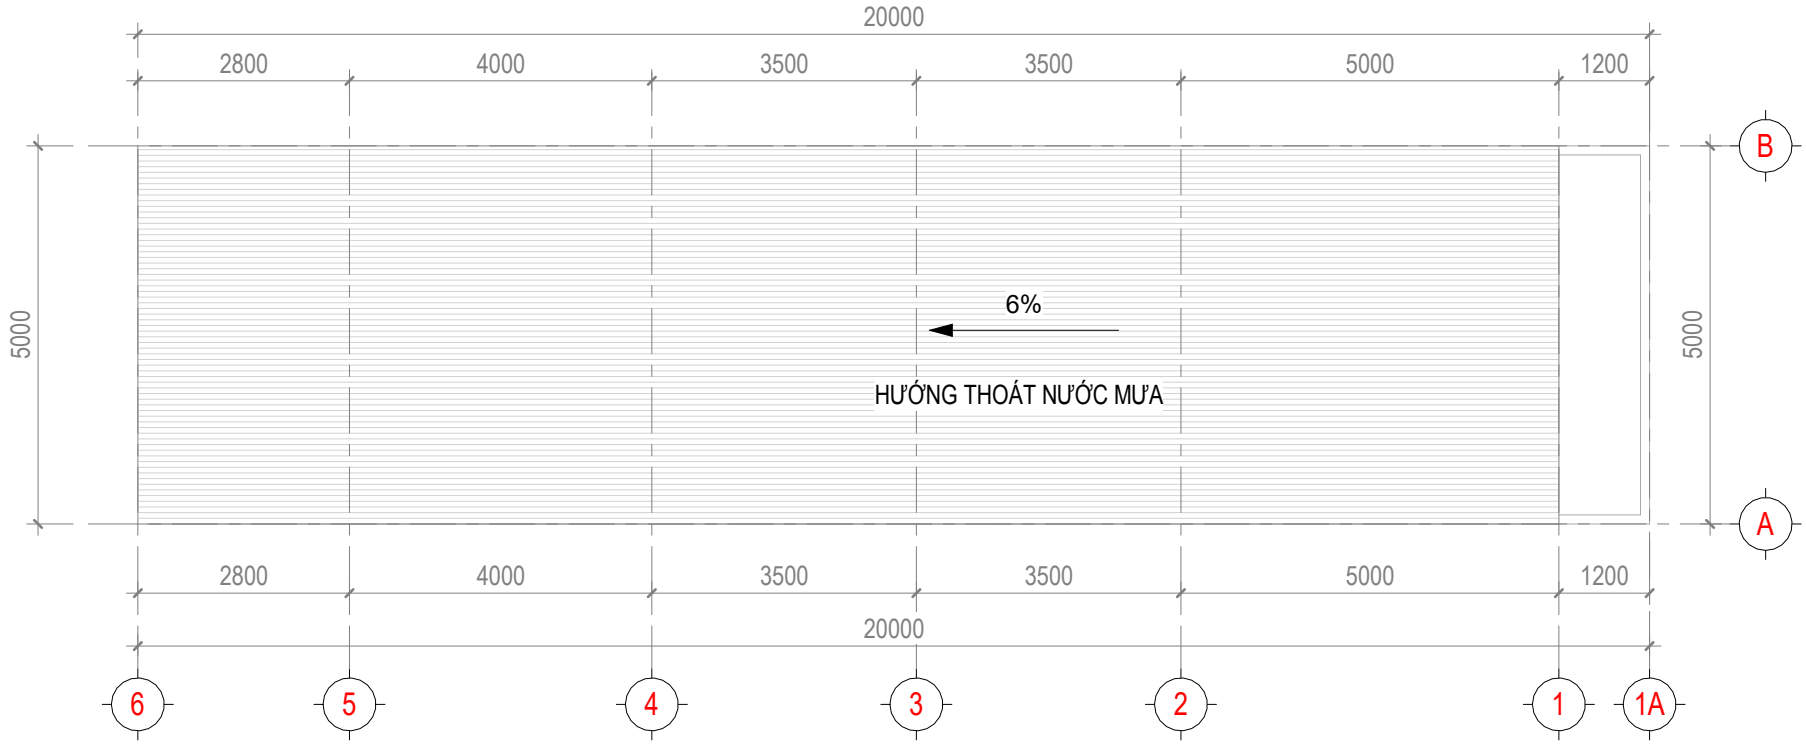

MẶT CẤP THOÁT NƯỚC MÁI

TL 1 : 100

CÔNG TY TNHH THƯƠNG MẠI VÀ XÂY DỰNG
PV INCONS

Địa chỉ: P007, Đường Lý Thái Tổ, phường Hưng Phú, thành phố Cần Thơ

Điện thoại: (+84) 0722 194 789 - 0939 751 194

GIÁM ĐỐC:	THIẾT KẾ:	CHỦ ĐẦU TƯ:	CÔNG TRÌNH:	TỶ LỆ:
TRẦN HOÀNG PHƯỚC	KS. TRẦN HOÀNG PHƯỚC	HÀ THU THẢO	NHÀ Ở RIÊNG LẺ ĐỊA ĐIỂM XÂY DỰNG: THỬA ĐẤT SỐ 1299, TỜ BẢN ĐỒ SỐ 10, ẤP TRƯỜNG THỌ 2, XÃ TRƯỜNG LONG, THÀNH PHỐ CẦN THƠ	A4 - 1:1 NGÀY: 03/08/2026 SỐ BẢN VẼ: CP-10