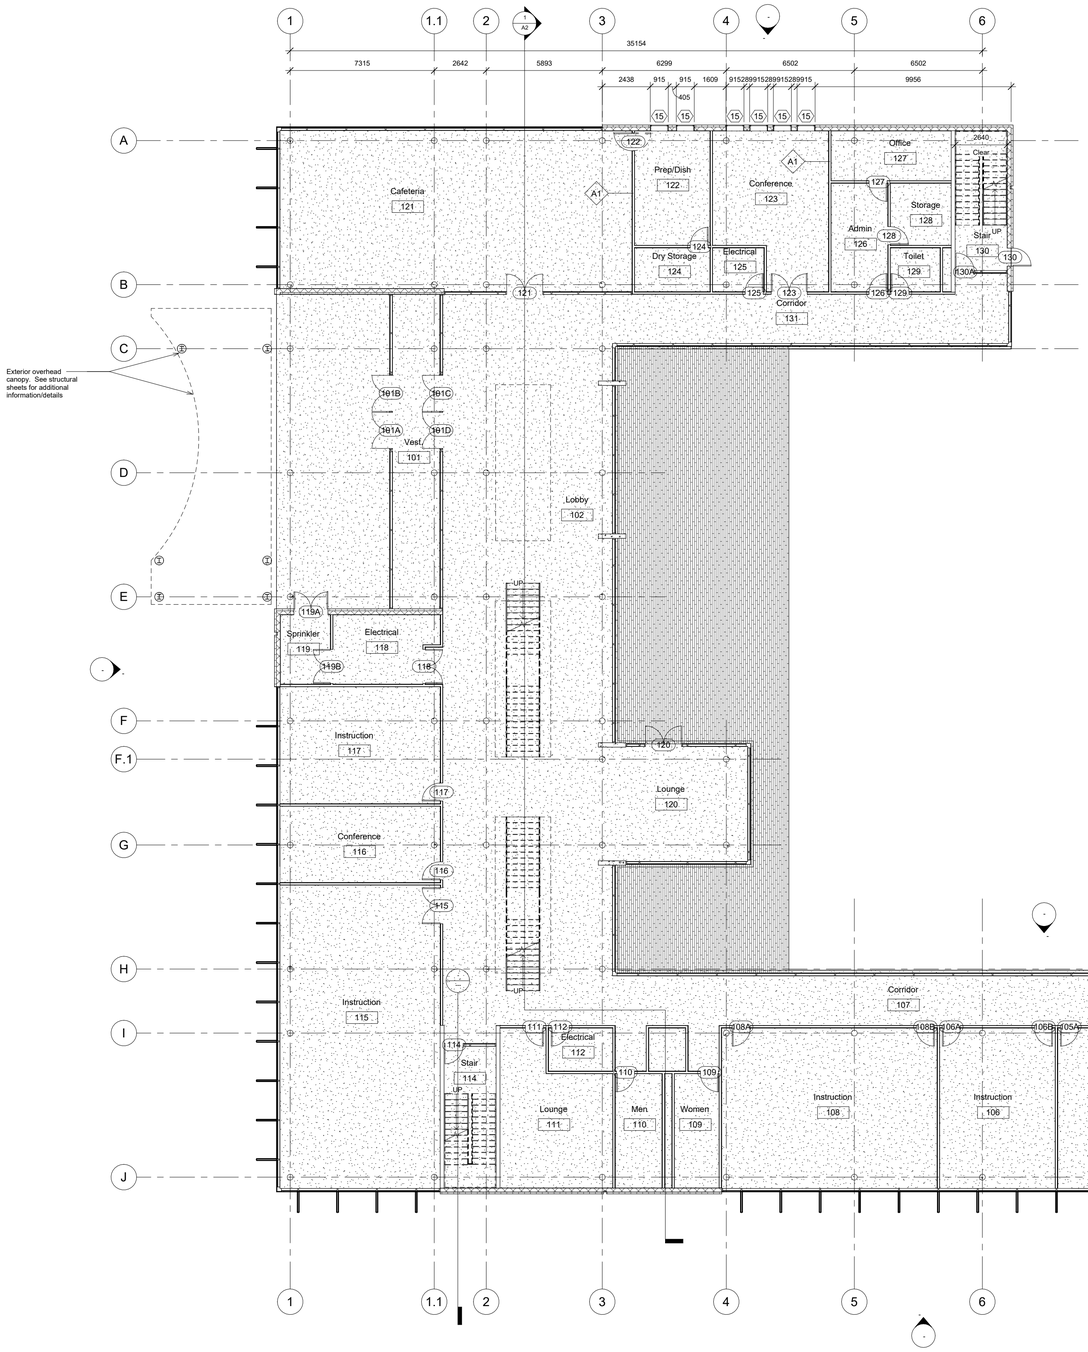


1 01 - Entry Level
1 : 100

AUTODESK.

www.autodesk.com/revit

Consultant
Address
Address
Phone
Fax
e-mail

Consultant
Address
Address
Phone
Fax
e-mail

Consultant
Address
Address
Phone
Fax
e-mail

Consultant
Address
Address
Phone
Fax
e-mail

Consultant
Address
Address
Phone
Fax
e-mail

No.	Description	Date


Owner

Project Name


Floor Plan

Project number	Project Number
Date	Issue Date
Drawn by	Author
Checked by	Checker


CHỮ KÝ SỐ
Ký bởi: TRẦN HOÀNG PHƯỚC
Ngày ký: 07/11/2026 16:23:46 (UTC+7)
Số CTS: 54010101A6603FD5476D8F52E709D184

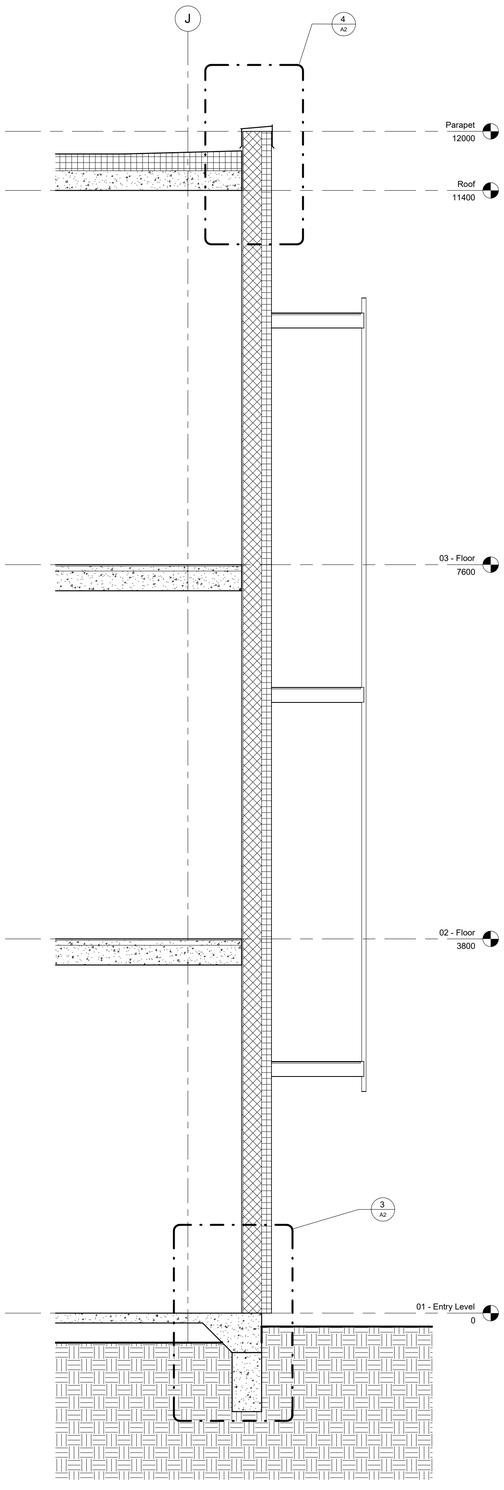


2 Typical Wall Section
1 : 20

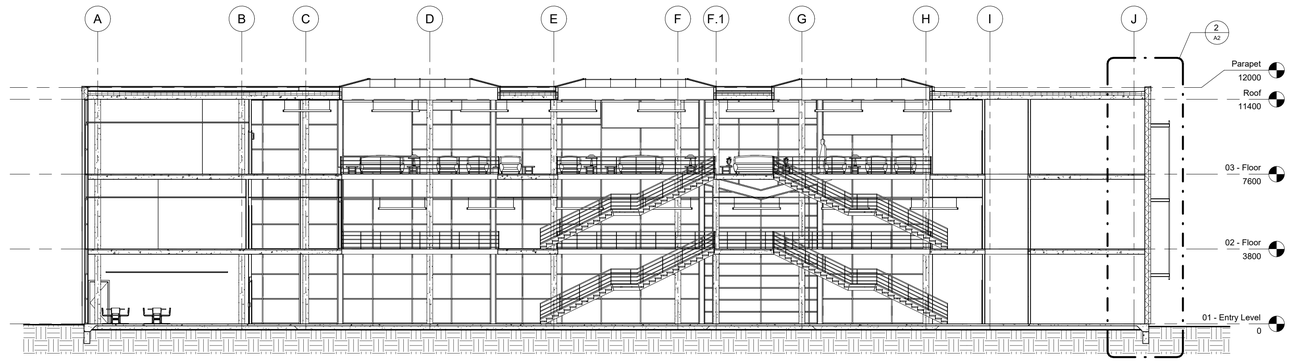

1 Section Through Main Stair
1 : 100

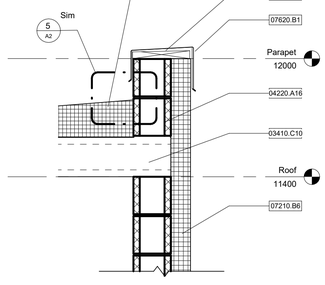


4 Detail At Parapet
1 : 10

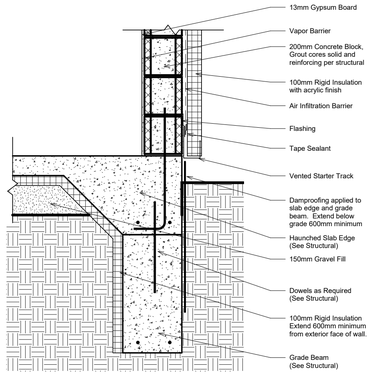

3 Detail At Grade
1 : 10

NOTES:
1. POLYMER OR METAL BATTEN STRIP ACCEPTABLE FOR WOOD OR METAL SUBSTRATE. METAL BATTEN MUST BE USED WITH MASONRY SUBSTRATE.

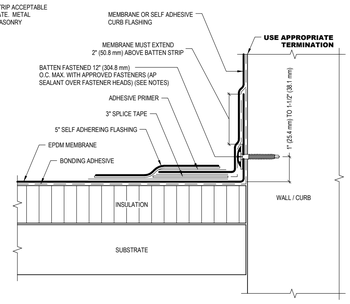

5 Roofing Termination Detail
1 : 2

AUTODESK.

www.autodesk.com/revit

Consultant
Address
Address
Phone
Fax
e-mail

Consultant
Address
Address
Phone
Fax
e-mail

Consultant
Address
Address
Phone
Fax
e-mail

Consultant
Address
Address
Phone
Fax
e-mail

Consultant
Address
Address
Phone
Fax
e-mail

No.	Description	Date

Owner

Project Name

Sections

Project number	Project Number
Date	Issue Date
Drawn by	Author
Checked by	Checker
	A2
Scale	As indicated

5/11/2026 2:28:47 pm