

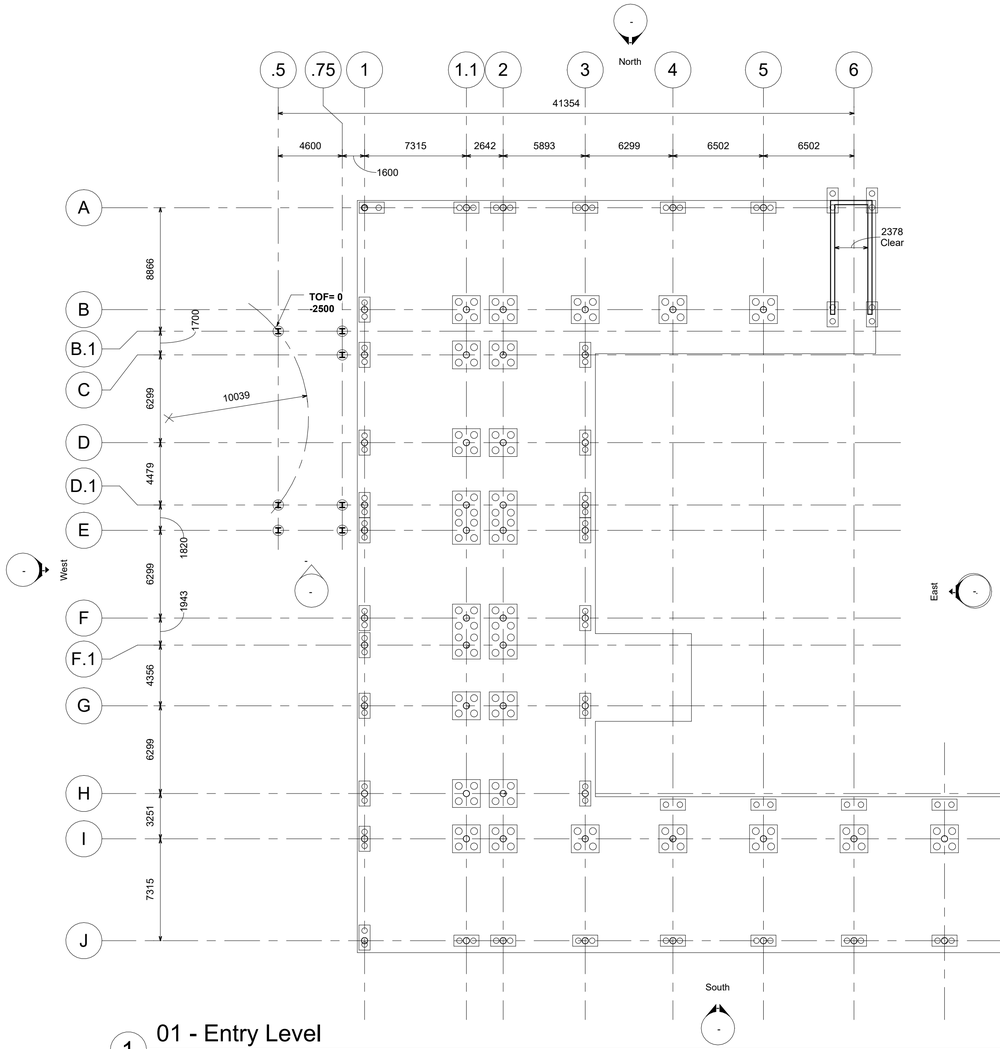


1 01 - Entry Level
1 : 200

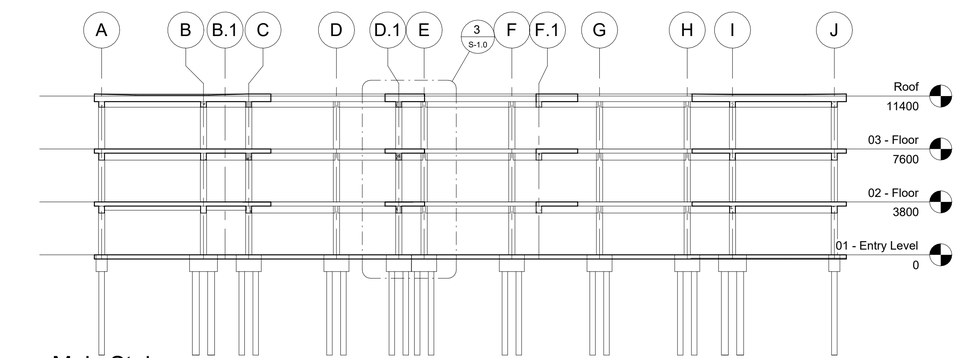

2 Main Stair
1 : 200

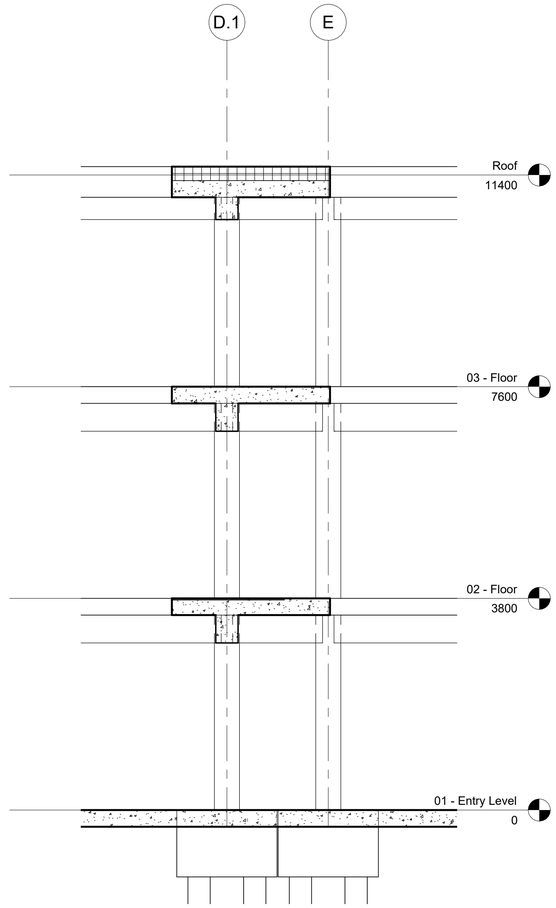

3 Typical Column Detail
1 : 50

Level Marker (Level name/Elevation)

Span Direction Fixed: 12.5mm

1i Rebar Tag

0 Grid Head Circle

Spot Elevation: Exterior Fixed

1 View Name
View Scale

View Name/scale

Symbol Legend
1 : 50

AUTODESK.

www.autodesk.com/revit

Consultant
Address
Address
Phone
Fax
e-mail

Consultant
Address
Address
Phone
Fax
e-mail

Consultant
Address
Address
Phone
Fax
e-mail

Consultant
Address
Address
Phone
Fax
e-mail

No.	Description	Date

J. Smith

Technical School

Plans and Elevations

Project number	2009-01
Date	01 April 2009
Drawn by	Author
Checked by	Checker

5 pm

CHỮ KÝ SỐ
Ký bởi: TRẦN HOÀNG PHƯỚC
Ngày ký: 07/11/2026 16:22:38 (UTC+7)
Số CTS: 54010101A6603FD5476D8F52E709D184

Structural Column Schedule

03 - Floor	450mm	450mm	450mm	450mm	450mm	450mm	450mm	450mm	450mm	450mm	**03 - Floor**
7600 **02 - Floor**	450mm	450mm	450mm	450mm	450mm	450mm	450mm	450mm	450mm	450mm	**7600** **02 - Floor**
3800 **01 - Entry Level**	450mm	450mm	450mm	450mm	450mm	450mm	450mm	450mm	450mm	450mm	**3800** **01 - Entry Level**
0 **Sub Level**											**0** **Sub Level**
-2500											**-2500**
Column Locations	A-1	A-1.1	A-2	A-3	A-4	A-5	B-1	B-1.1	B-2	B-3	

AUTODESK.

www.autodesk.com/revit

Consultant
Address
Address
Phone
Fax
e-mail

Consultant
Address
Address
Phone
Fax
e-mail

Consultant
Address
Address
Phone
Fax
e-mail

Consultant
Address
Address
Phone
Fax
e-mail

No.	Description	Date

J. Smith

Technical School


Graphical Column Schedule

Project number	2009-01
Date	01 April 2009
Drawn by	Author
Checked by	Checker


S-2.0

Scale 1 : 100


5/11/2026 2:31:26 pm

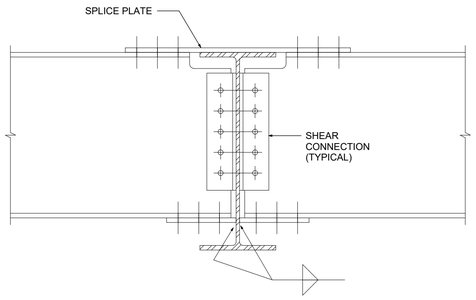

1 TYPICAL BOLTED MOMENT CONNECTION
NO SCALE

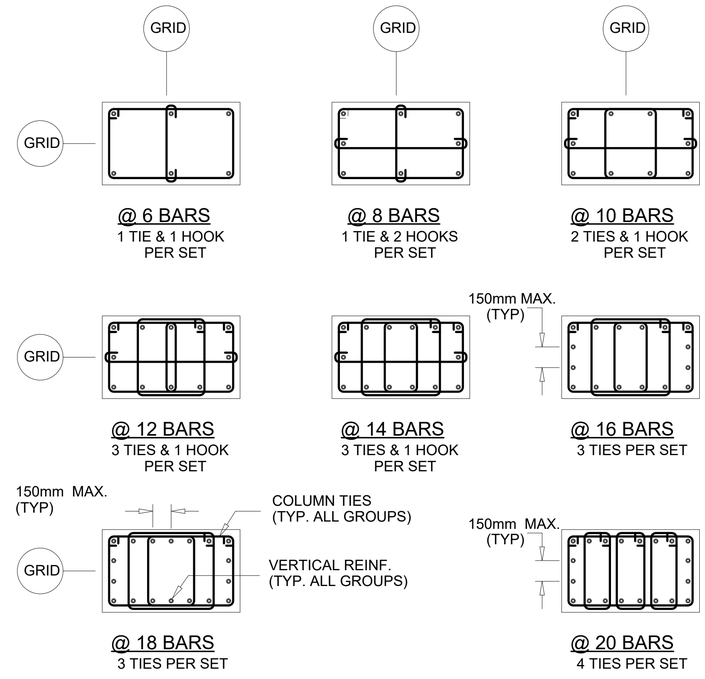

2 TYPICAL RECTANGULAR COLUMN TIES
NO SCALE

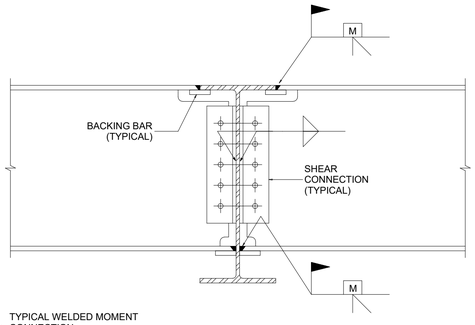

3 TYPICAL WELDED MOMENT CONNECTION
NO SCALE

AUTODESK.

www.autodesk.com/revit

Consultant
Address
Address
Address
Phone

Consultant
Address
Address
Address
Phone

Consultant
Address
Address
Address
Phone

Consultant
Address
Address
Address
Phone

Consultant
Address
Address
Address
Phone

No.	Description	Date

J. Smith

Technical School

Typical Details

Project Number	2009-01
Date	01 April 2009
Drawn By	Author
Checked By	Checker

S-3.0

Scale 1 : 4

5/11/2026 2:31:27 pm